
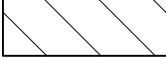
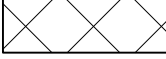


ΤΟ ΠΑΡΟΝ ΣΧΕΔΙΟ ΕΙΝΑΙ ΑΝΤΙΓΡΑΦΟ ΑΥΤΟΥ ΠΟΥ ΕΧΕΙ ΥΠΟΒΛΗΘΕΙ ΗΛΕΚΤΡΟΝΙΚΑ ΣΤΟ ΠΛΗΡΟΦΟΡΙΑΚΟ ΣΥΣΤΗΜΑ ΤΟΥ ΤΕΕ & ΤΟ ΟΠΟΙΟ ΣΥΝΟΔΕΥΕΙ ΤΗΝ ΥΠΑΓΓΡΑΦΗ 11356428/23-01-2020 ΔΗΛΩΣΗ ΤΟΥ Ν.4495/2017 ΜΕ ΗΛΕΚΤΡΟΝΙΚΟ ΚΩΔΙΚΟ 385Α0Ε0F838ΑD53D. ΕΧΟΥΝ ΥΠΟΒΛΗΘΕΙ ΟΛΑ ΤΑ ΑΠΑΡΑΙΤΗΤΑ ΔΙΚΑΙΟΛΟΓΗΤΙΚΑ ΚΑΙ ΜΕΛΕΤΕΣ ΠΟΥ ΑΠΑΙΤΟΥΝΤΑΙ ΣΤΟΝ Ν.4495/2017.

	ΧΩΡΟΙ	ΕΜΒΑΔΟΝ Μ2
	ΤΜΗΜΑ ΙΣΟΓΕΙΟΥ ΝΟΜΙΣΜΟΣ ΥΦΙΣΤΑΜΕΝΟ ΣΥΜΦΩΝΑ ΜΕ ΤΗΝ ΥΠΑΓΙΟΡΙΜ. 1606/90 ΟΙΚ. ΑΔΕΙΑ	48.50
	ΕΠΕΚΤΑΣΗ ΙΣΟΓΕΙΟΥ ΚΑΤΟΙΚΙΑΣ ΚΑΤΑΣΚΕΥΑΣΜΕΝΗ ΑΥΘΑΙΡΕΤΑ ΚΑΙ ΤΑΚΤΟΠΟΙΗΜΕΝΗ ΣΥΜΦΩΝΑ ΜΕ ΤΗΝ ΥΠΑΓΙΟΡΙΜ. 11356428/23-01-2020 ΔΗΛΩΣΗ ΤΟΥ Ν.4495/2017	27.77
	ΜΕΤΑΤΡΟΠΗ Η/Χ ΙΣΟΓΕΙΟΥ ΣΕ ΚΑΤΟΙΚΙΑ ΚΑΤΑΣΚΕΥΑΣΜΕΝΗ ΑΥΘΑΙΡΕΤΑ ΚΑΙ ΤΑΚΤΟΠΟΙΗΜΕΝΗ ΣΥΜΦΩΝΑ ΜΕ ΤΗΝ ΥΠΑΓΙΟΡΙΜ. 11356428/23-01-2020 ΔΗΛΩΣΗ ΤΟΥ Ν.4495/2017	6.75
	ΣΥΝΟΛΙΚΟ ΕΜΒΑΔΟ ΙΣΟΓΕΙΟΥ ΚΑΤΟΙΚΙΑΣ	83.02
	ΛΟΠΙΣ ΠΟΛΥΩΟΔΙΚΗΣ ΠΑΡΑΒΑΣΕΙΣ (ΚΑΤΑΣΚΕΥΗ ΑΠΟΘΗΚΗΣ/ΕΒΗΤΟΣΤΑΣΙΟΥ ΕΜΒ. 13,68 Μ2, ΚΑΤΑΣΚΕΥΗ ΑΠΟΘΗΚΗΣ ΚΤΙΡΙΟΥ Β ΕΜΒ. 6,44 Μ2, ΕΚΧΩΜΑΤΩΣΗ ΠΕΡΙΒΑΛΛΟΝΤΟΣ ΧΩΡΟΥ, ΜΕΤΑΒΑΘΕΙΣ ΣΕ ΕΞΟΤΕΣ, ΔΙΑΜΟΡΦΩΣΗ ΠΕΡΙΒΑΛΛΟΝΤΟΣ ΧΩΡΟΥ, ΜΕΤΑΒΑΘΕΙΣ ΣΕ ΑΝΟΙΓΜΑΤΑ, ΚΑΤΑΣΚΕΥΗ ΚΛΙΜΑΚΙΩΝ) ΚΑΤΑΣΚΕΥΑΣΜΕΝΗ ΑΥΘΑΙΡΕΤΑ ΚΑΙ ΤΑΚΤΟΠΟΙΗΜΕΝΗΣ ΣΥΜΦΩΝΑ ΜΕ ΤΗΝ ΥΠΑΓΙΟΡΙΜ. 11356428/23-01-2020 ΔΗΛΩΣΗ ΤΟΥ Ν.4495/2017	

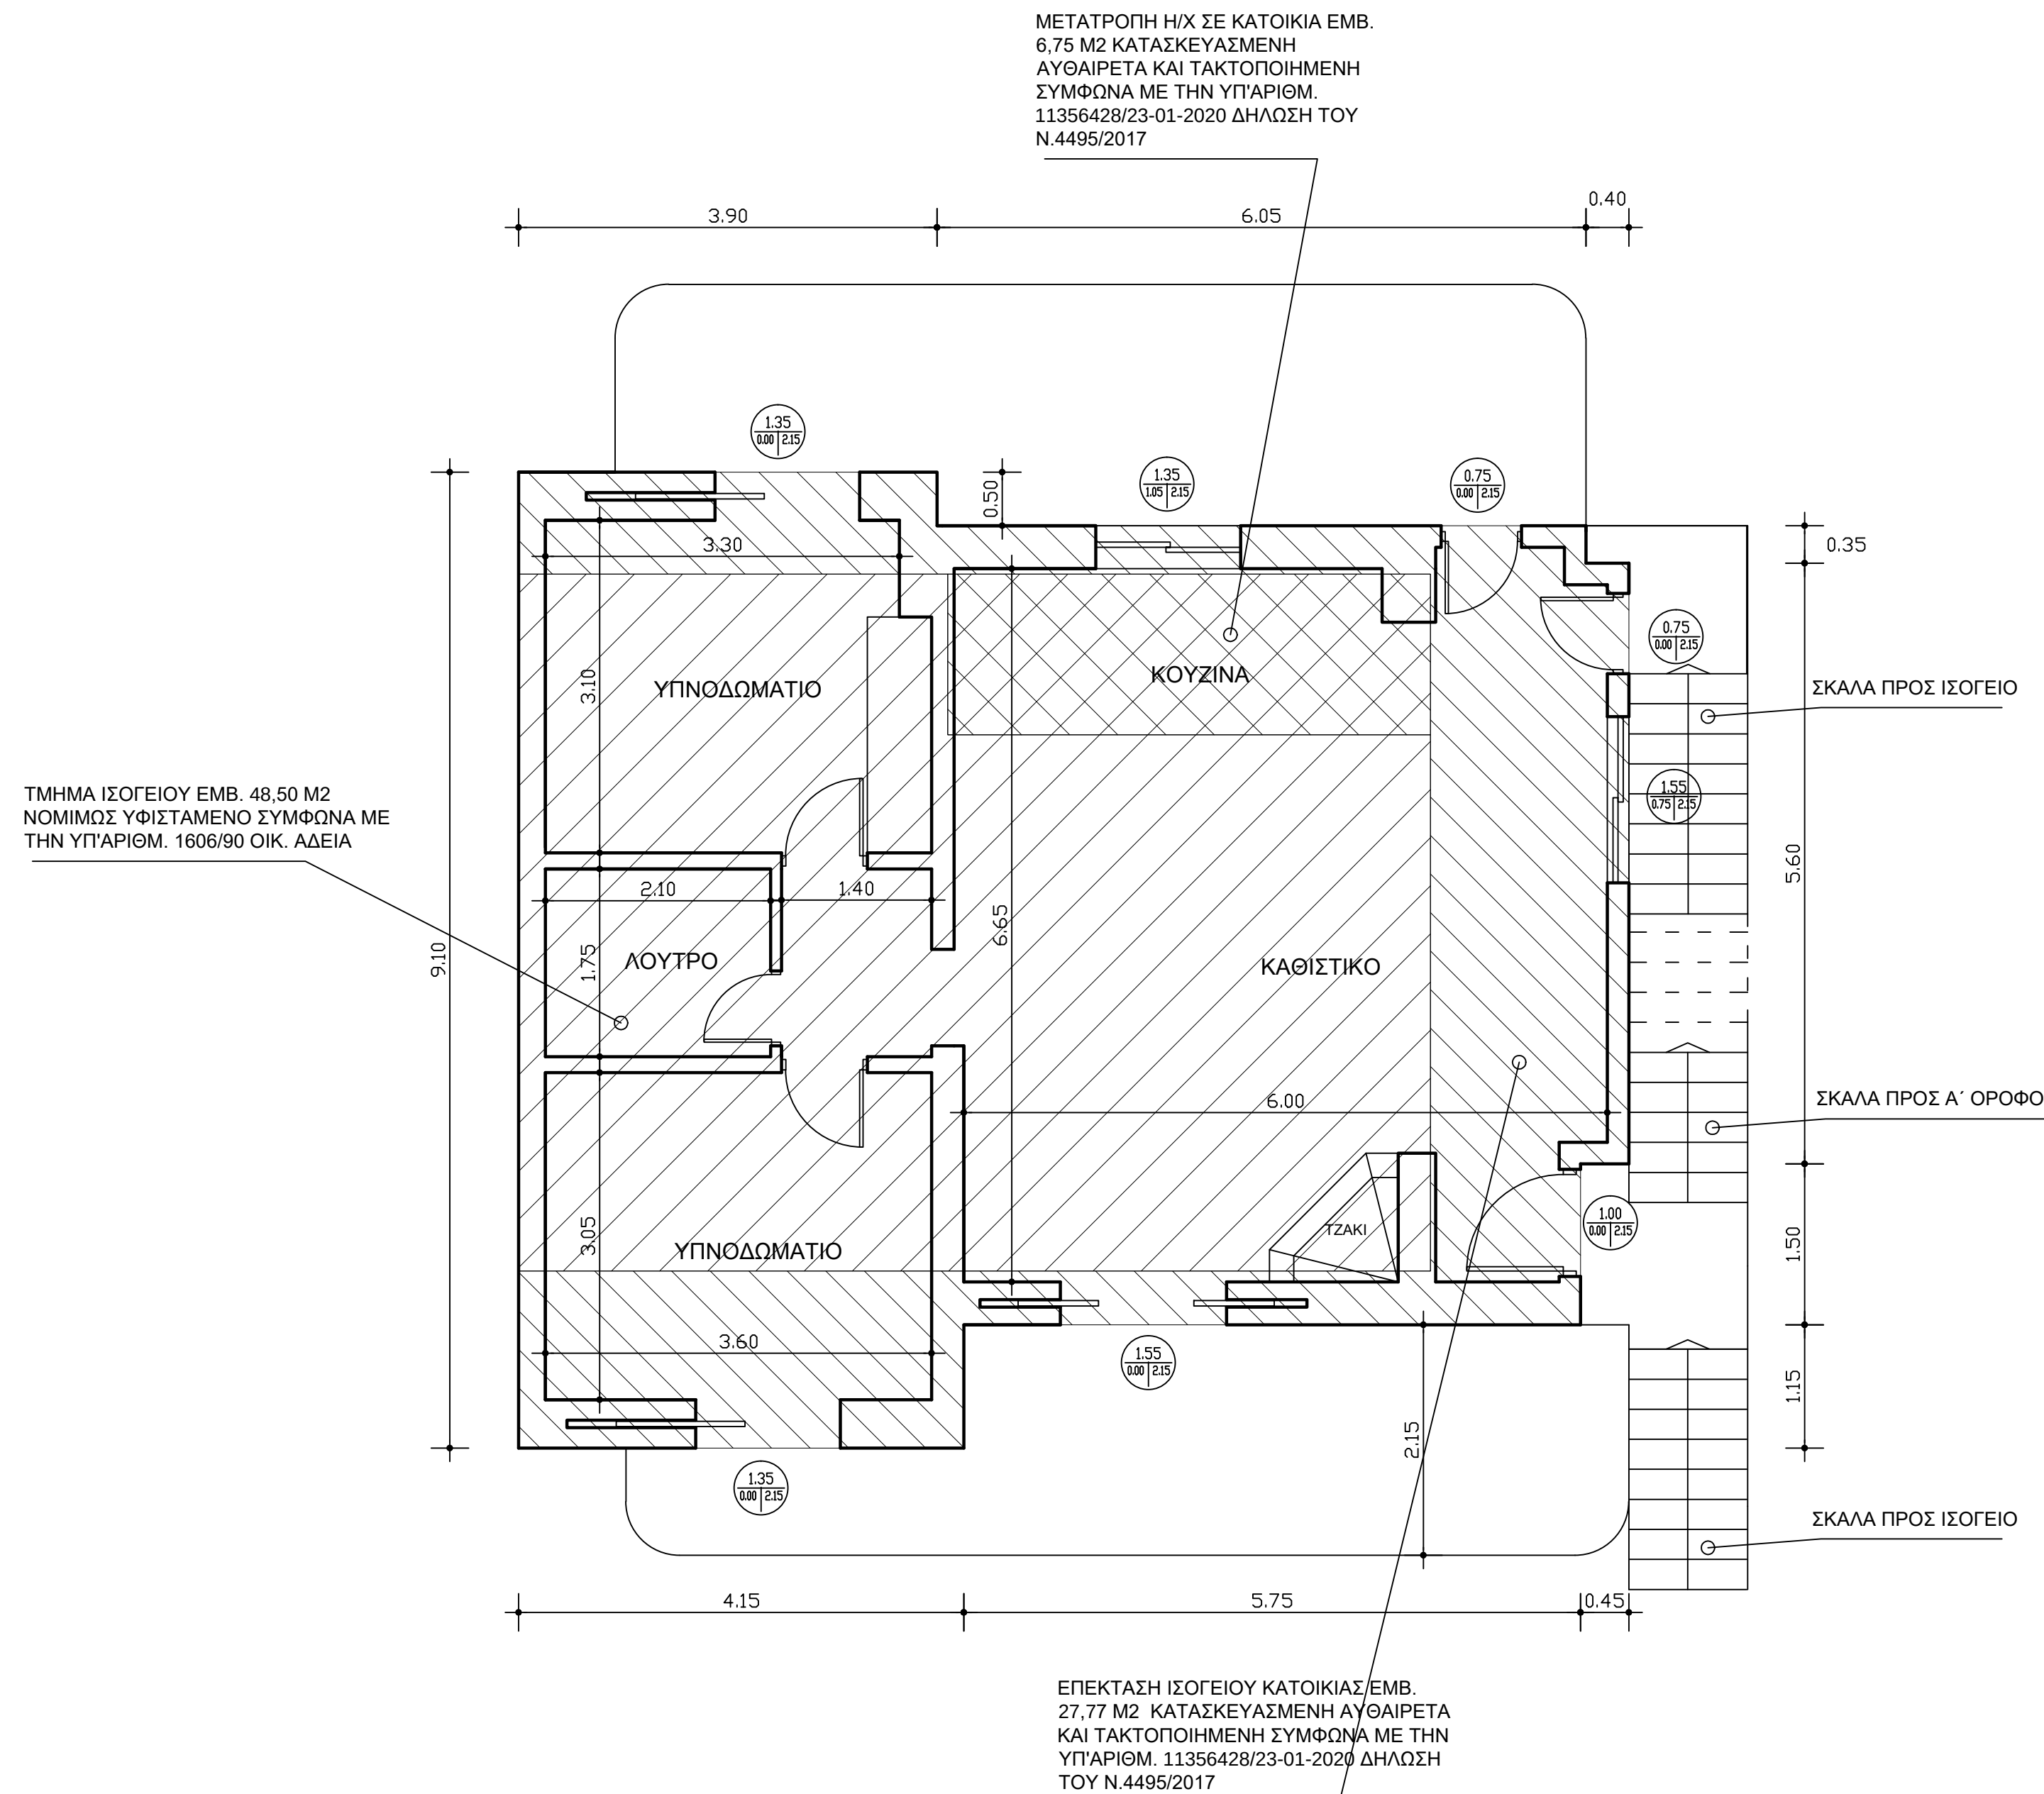

ΕΡΓΟ ΤΑΚΤΟΠΟΙΗΣΗ ΑΥΘΑΙΡΕΤΩΝ ΚΑΤΑΣΚΕΥΩΝ ΣΥΜΦΩΝΑ
ΜΕ ΤΟΝ Ν.4495/2017

ΘΕΣΗ ΘΕΜΙΣΤΟΚΛΕΟΥΣ 8-10,
Δ.Ε. ΑΡΤΕΜΙΔΟΣ, ΔΗΜΟΣ ΣΠΑΤΩΝ-ΑΡΤΕΜΙΔΟΣ

ΕΡΓΟΔΟΤΗΣ ΑΙΚΑΤΕΡΙΝΗ ΜΠΑΡΜΠΑΡΗ

ΘΕΜΑ	ΚΑΤΟΨΗ ΙΣΟΓΕΙΟΥ ΚΤΙΡΙΟΥ Α
------	---------------------------

A₂

1:50

ΚΩΝΣΤΑΝΤΙΝΟΣ ΑΛ. ΝΑΣΤΟΣ
ΠΟΛΙΤΙΚΟΣ ΜΗΧΑΝΙΚΟΣ Ε.Μ.Π.
ΑΡΙΘΜΟΣ ΜΗΤΡΩΟΥ Τ.Ε.Ε. 98103
Λ. ΑΡΤΕΜΙΔΟΣ & ΠΑΧΥΔΑΦΝΗΣ ΑΡΤΕΜΙΣ - Τ.Κ. 19016
ΑΦΜ: 062574895 ΔΟΥ ΠΑΛΛΗΝΗΣ
ΤΗΛ : 2194082214

MHXANIKOY